
Section A - long section on the centerline

Fin depths assumed 7" flue / 4" filter below the rim - measure with the pan seated.

Scale 1:16 (3/4" = 1'-0")
Tags A1-A27

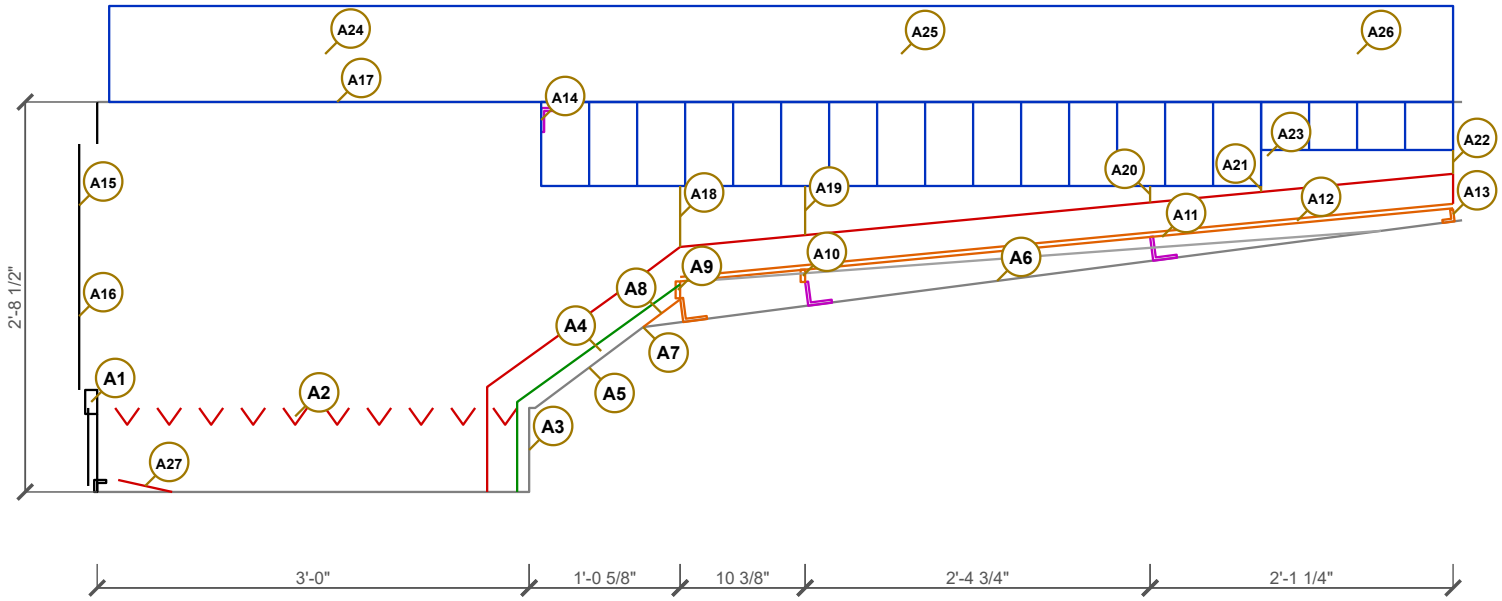


A1 EXIST. FRONT CROSS BRACE - STAYS
A2 GRATES 2x2x1/4, POINT DOWN, FILL WITH ASH
A3 FIREBOX BACK VERTICAL TO GRATE HT
A4 1" RIGID CERAMIC BOARD ON THE STEEL, THEN 2.5" BRICK, MORTARED
A5 EXIST. RAMP, 2x2 ANGLE FRAME, ~37 DEG
A6 EXIST. FLOOR ON LONG 2x2 ANGLES, ONE STRAIGHT PIECE, TOP OF RAMP TO BACK
A7 TOP OF OLD RAMP (2x2 ANGLE FRAME) - NEW PLATE STARTS HERE
A8 NEW 3/16 RAMP STRIP, 38 x 4, CONTINUES OLD RAMP ~37 DEG
A9 NEW BRACE STA 48.62: 2x2x1/4 x 38 ON FLOOR + 2x3/8 x 38 STRIP
A10 EXIST. BRACE 59 (TOP 15 BELOW RIM) + 1" FLAT
A11 EXIST. BRACE 87.75 (TOP 11.25 BELOW RIM) - BARS ON TOP, AS IS
A12 2x3/8 FLAT, 5 @ 9.06 OC, ~65" ONE PIECE
A13 NEW REAR SUPPORT: 1x1x1/4 ANGLE IN BACK BOTTOM CORNER, ~0.12" SHIM
A14 EXIST. BRACE UNDER FINISH PAN AT STA 37 - LOCATION NOT MEASURED
A15 DOOR LINER: 1 IN. BOARD + FLOATING 3/16 PLATE 28 x 21 ON 304 STUDS
A16 DOOR ROPE GASKET 3/4 GRAPHITE, IN DOOR LIP
A17 PAN RAIL GASKET 1/4 x 1-1/2 TAPE ON EXIST. RIM
A18 STA 48.58: 5.12" BRICK TO FIN
A19 STA 59: 4.12" BRICK TO FIN
A20 STA 87.75: 1.38" BRICK TO FIN
A21 STA 97: 0.5" BRICK TO FIN
A22 STA 113: 2" BRICK TO FIN
A23 STA 97: 3.5" UNDER FILTER FINS
A24 FINISH PAN
A25 FLUE PAN
A26 FILTER PAN
A27 FRONT COURSE OF ASH PIT FLOOR CUT TO A WEDGE: FLOOR UP TO SILL TOP, RAKE SLIDES OUT

Front elevation

Looking at the front of the arch.

Scale 1:12 (1" = 1'-0")
Tags F1-F10

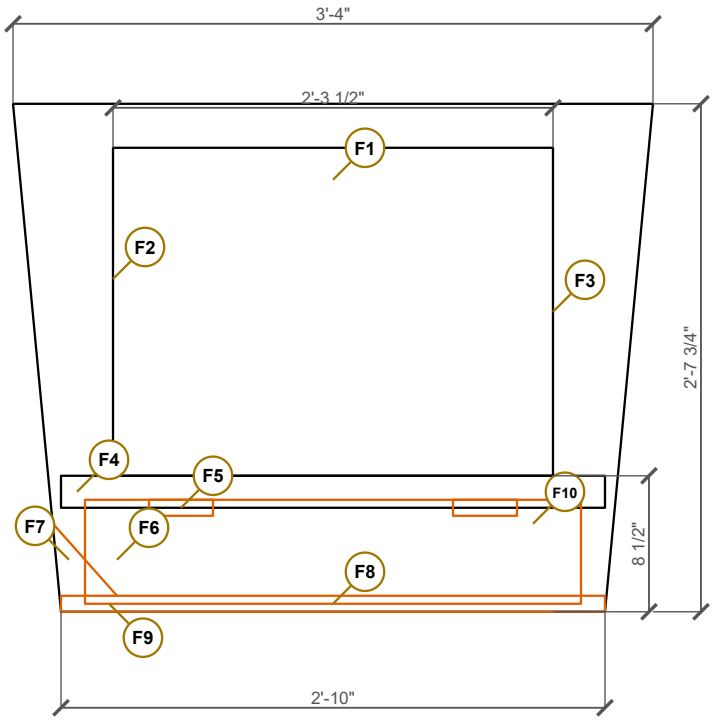


F1	FIRE DOOR OPENING 27.5 x 20.5, HINGED LEFT
F2	NEW DOOR FRAME 2x2x1/4: SIDES 22, TOP 31-1/2 (IF EXIST. FRAME TOO WARPED)
F3	CAM/WEDGE LATCH + SPRING HANDLE, RIGHT SIDE
F4	EXIST. CROSS BRACE - STAYS
F5	BARREL HINGES (2), 4-6 IN., 5/8 PIN
F6	LOUVER 3/16 PLATE ~31 x 6.5, FIELD-FIT
F7	QUADRANT ARM 1/4 x 1-1/2 x 10, LEFT SIDE (AWAY FROM LATCH)
F8	LOUVER STIFFENER 1x1x1/4 x 31 + SPRING HANDLE
F9	NEW SILL 1x1x1/4 x 34 AT FLOOR - LOUVER STOP, TAPE GASKET ON IT
F10	LOUVER TAPE GASKET 1/8 x 1 (BRACE, SIDES, SILL)

Section B - back bays at station 70

Looking toward the chimney.

Scale 1:8 (1-1/2" = 1'-0")
Tags B1-B6

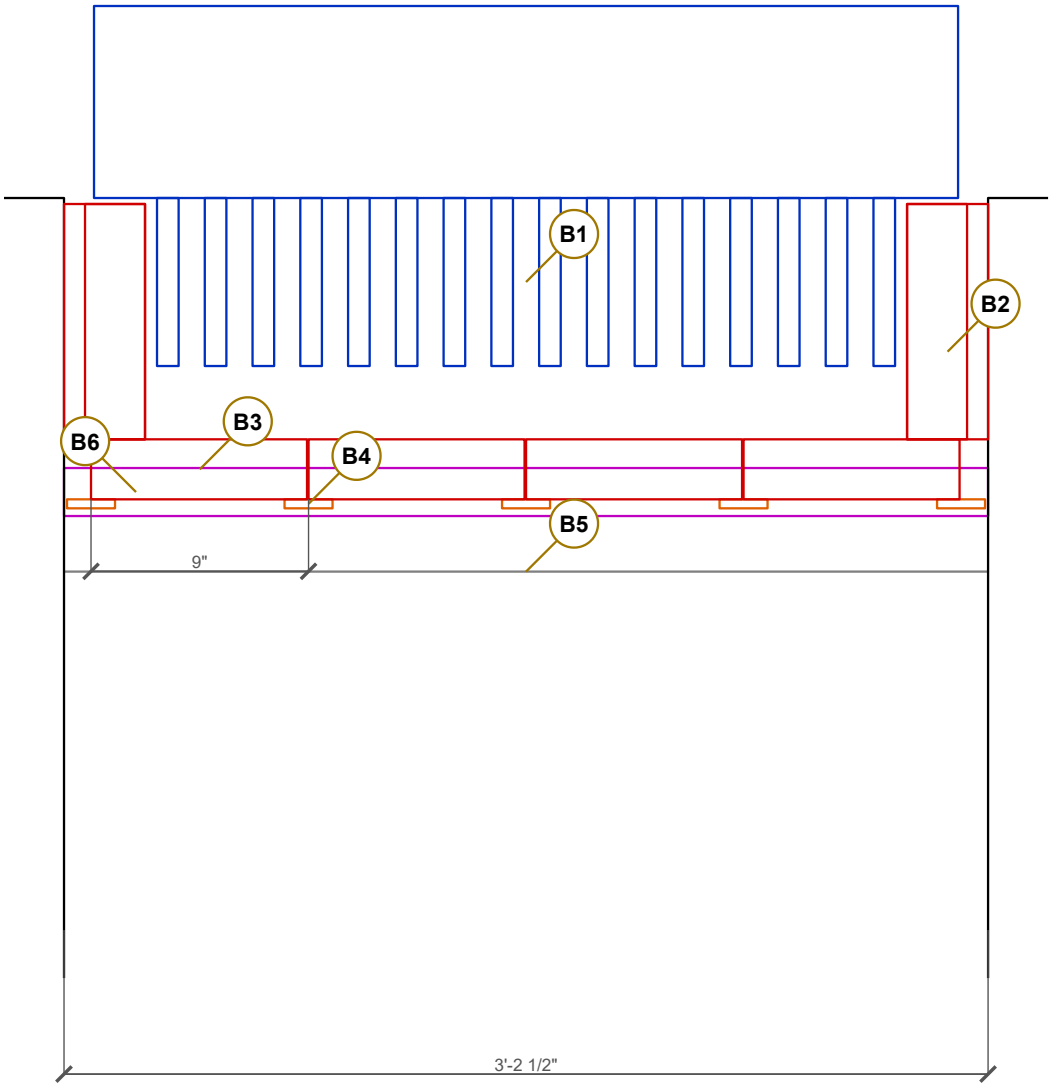

B1 FLUE PAN FINS

B2 BRICK ON EDGE + ~7/8 BLANKET, 3.38"/SIDE

B3 FULL BRICK LAID CROSSWISE

B4 5 BARS 2x3/8 @ 9.06 OC

B5 OLD FLOOR; PERLITE FILL BELOW BARS

B6 EXIST. BRACE 87.75 BEYOND, WALL TO WALL